

Legenda	
	Ar Condicionado tipo Split
	Bucha de redução longa
CAG	Caixa de areia pluvial c/grelha
CE	Caixas Inspeção Esgoto Simples
CG	Caixas de Gordura
	Chuveiro Residencial
	Curva 45 Longa para Esgoto Sanitário
	Curva 45 longa Amanco
	Curva 90 curta- coluna
	Joelho 45
	Junção simples
	Junção simples c/ redução
	Lavatório Residencial com sifão
	Máquina de Lavar Roupas DN 50mm
	Pia de Cozinha Residencial com Sifão 50mm
	Ramais de Ventilação
	Tanque de Lavar Roupas DN 40mm
	Vaso Sanitário c/ curva 90°

Lista de Materiais	
Esgoto	
Caixas de Passagem	
Caixa de gordura	
CG 60x60 cm	1 pç
Caixa de inspeção esgoto simples	
CE- 60x60 cm	4 pç
PVC Acessórios	
Caixa sifonada	
100x100x50	1 pç
150x150x50	1 pç
Sifão de copo p/ pia e lavatório	
1" - 1.1/2"	1 pç
1" - 2"	2 pç
Sifão flexível c/ Adaptador	
1.1/2" - 1.1/2"	1 pç
Válvula p/ lavatório e tanque	
1"	1 pç
Válvula p/ pia	
1"	2 pç
Válvula p/ tanque	
1 1/2"	1 pç
PVC Esgoto	
Curva 45 longa	
100 mm	5 pç
50 mm	4 pç
Curva 45 longa Amanco	
40 mm	1 pç
Curva 90 curta	
100 mm	3 pç
40 mm	2 pç
Joelho 45	
100 mm	1 pç
50 mm	1 pç
75 mm	1 pç
Joelho 90	
50 mm	7 pç
Joelho 90 c/anel p/ esgoto secundário	
40 mm - 1.1/2"	2 pç
Junção simples	
100 mm - 50 mm	1 pç
75 mm - 50 mm	1 pç
Redução excêntrica	
75 mm - 50 mm	1 pç
Tubo rígido c/ ponta lisa	
100 mm - 4"	55 m
40 mm	2.07 m
50 mm - 2"	8.44 m
75 mm - 3"	1.96 m
Tê sanitário	
50 mm - 50 mm	1 pç
Pluvial	
Caixas de Passagem	
Caixa de areia pluvial com grelha	
CAG- 60x60cm	1 pç
PVC Esgoto	
Bucha de redução longa	
50 mm - 40 mm	2 pç
Curva 45 longa	
100 mm	3 pç
50 mm	1 pç
75 mm	1 pç
Curva 45 longa Amanco	
40 mm	3 pç
Curva 90 curta	
100 mm	3 pç
40 mm	3 pç
50 mm	3 pç
75 mm	1 pç
Joelho 45	
100 mm	1 pç
75 mm	1 pç
Junção simples	
100 mm - 50 mm	4 pç
40 mm x 40 mm	1 pç
50 mm - 50 mm	1 pç
Tubo rígido c/ ponta lisa	
100 mm - 4"	67.59 m
40 mm	13.43 m
50 mm - 2"	4.47 m
75 mm - 3"	4.34 m
PVC misto soldável	
Luva soldável c/ rosca	
25 mm -3/4"	2 pç
PVC rígido soldável	
Bucha de redução sold. longa	
40 mm - 25 mm	2 pç
Curva de transposição	
25 mm	2 pç
Joelho 90° soldável	
25 mm	4 pç
Tubos	
25 mm	12 m
Ventilação	
PVC Esgoto	
Curva 45 longa	
50 mm	1 pç
Curva 90 curta	
50 mm	1 pç
Tubo rígido c/ ponta lisa	
50 mm - 2"	0.34 m

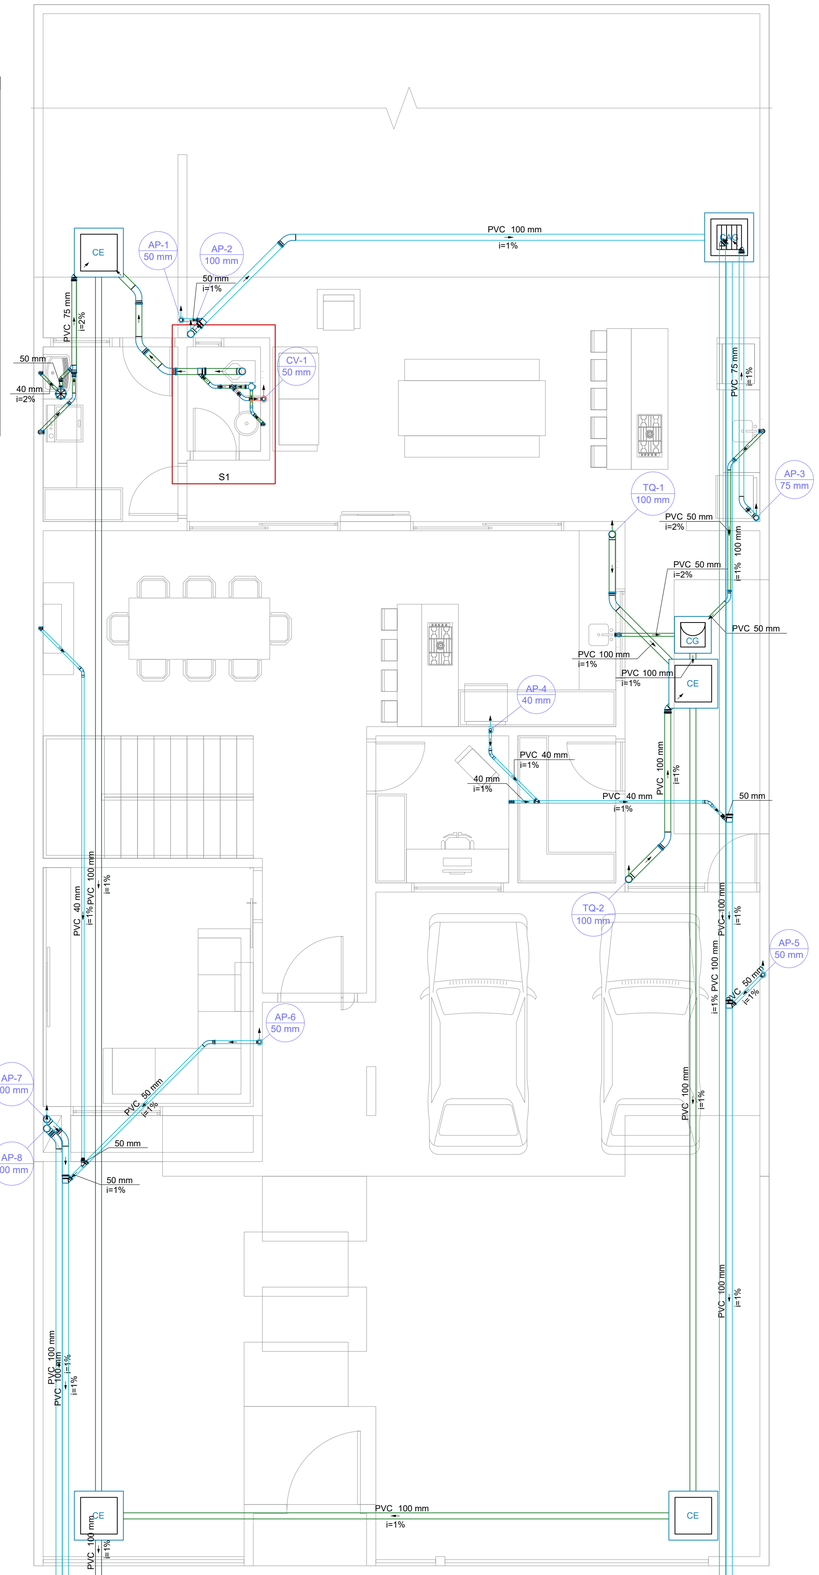


PLANTA TERREO - SANITÁRIO/PLUVIAL
Escala 1:50

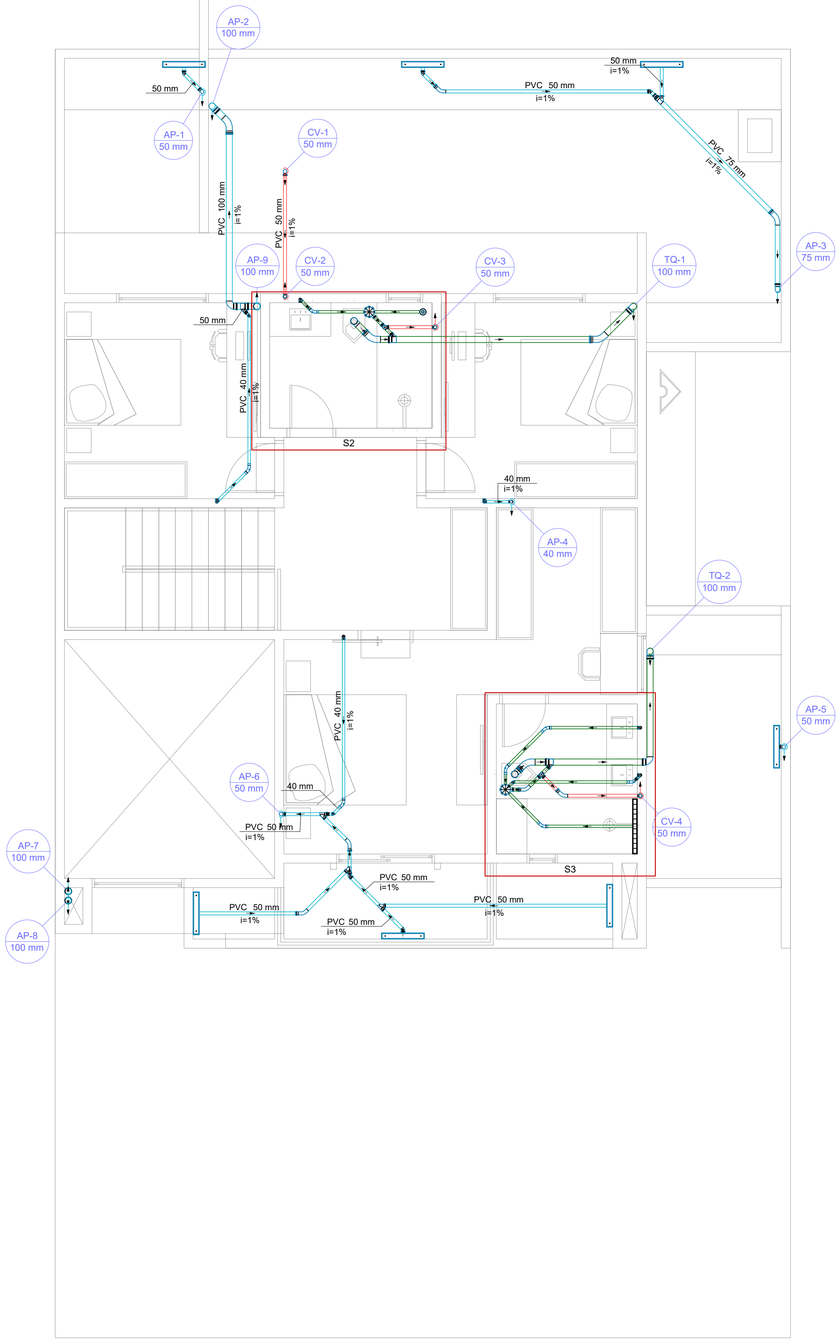

PLANTA SUPERIOR - SANITÁRIO/PLUVIAL
Escala 1:50


Lista de Materiais	
Esgoto	
PVC Acessórios	
Caixa sifonada	
150x150x50	2 pç
Ralo linear c/ grelha	
90 cm	1 pç
Ralo sifonado alt. reg. saída 40	
100 mm - 40 mm	1 pç
Sifão de copo p/ pia e lavatório	
1" - 1.1/2"	3 pç
Válvula p/ lavatório e tanque	
1"	3 pç
PVC Esgoto	
Curva 45 longa	
100 mm	3 pç
50 mm	1 pç
Curva 45 longa Amanco	
40 mm	5 pç
Curva 90 curta	
100 mm	5 pç
40 mm	4 pç
Joelho 45	
40 mm	1 pç
Joelho 90	
50 mm	2 pç
Joelho 90 c/anel p/ esgoto secundário	
40 mm - 1.1/2"	3 pç
Junção simples	
100 mm - 50 mm	2 pç
Tubo rígido c/ ponta lisa	
100 mm - 4"	14.15 m
40 mm	9.99 m
50 mm - 2"	0.81 m
Tê sanitário	
50 mm - 50 mm	2 pç

Lista de Materiais	
Pluvial	
PVC Acessórios	
Ralo linear c/ grelha	
70 cm	7 pç
PVC Esgoto	
Bucha de redução longa	
50 mm - 40 mm	2 pç
Curva 45 longa	
100 mm	1 pç
50 mm	3 pç
75 mm	1 pç
Curva 45 longa Amanco	
40 mm	2 pç
Curva 90 curta	
100 mm	3 pç
40 mm	4 pç
50 mm	3 pç
75 mm	1 pç
Joelho 45	
40 mm	2 pç
50 mm	5 pç
Junção simples	
100 mm - 50 mm	1 pç
50 mm - 50 mm	3 pç
75 mm - 50 mm	1 pç
Luva simples	
100 mm	2 pç
Redução excêntrica	
75 mm - 50 mm	1 pç
Tubo rígido c/ ponta lisa	
100 mm - 4"	13.86 m
40 mm	10.33 m
50 mm - 2"	18.92 m
75 mm - 3"	6.53 m
PVC misto soldável	
Luva soldável c/ rosca	
25 mm -3/4"	3 pç
PVC rígido soldável	
Bucha de redução sold. longa	
40 mm - 25 mm	3 pç
Curva de transposição	
25 mm	3 pç
Joelho 90° soldável	
25 mm	6 pç
Tubos	
25 mm	18 m
Ventilação	
PVC Esgoto	
Curva 45 longa	
50 mm	1 pç
Curva 90 curta	
50 mm	4 pç
Tubo rígido c/ ponta lisa	
50 mm - 2"	7.71 m

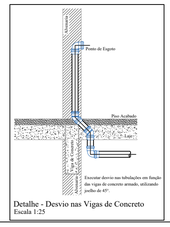


Detalhe - Desvio nas Vigas de Concreto
Escala 1:25

CAIXA DE INSPEÇÃO - GENÉRICA

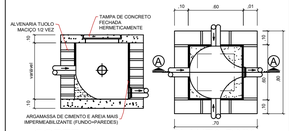

Escala 1:20 Escala 1:20

CAIXA DE GORDURA - GENÉRICA

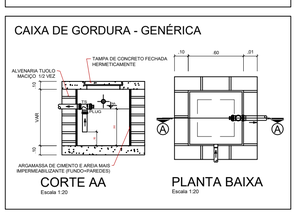

Escala 1:20 Escala 1:20

Legenda	
	Ar Condicionado tipo Split
	Bucha de redução longa
	Chuveiro Residencial
	Curva 45 Longa para Esgoto Sanitário
	Curva 45 longa Amanco
	Curva 90 curta
	Curva 90 curta- coluna
	Curva 90 curta- desce
	Joelho 45
	Junção simples
	Junção simples c/ redução
	Lavatório Residencial com sifão
	Luva simples- coluna
RL	
	Ramais de Ventilação
	Vaso Sanitário c/ curva 90°

INSTALAÇÕES PREDIAIS DE ESGOTO SANITÁRIO

* TUBOS E CONEXÕES EM PVC RÍGIDO, NA COR BRANCA, PARA INSTALAÇÕES PREDIAIS DE ESGOTO SANITÁRIO E VENTILAÇÃO, FABRICADOS DE ACORDO COM A ESPECIFICAÇÃO BRASILEIRA EB608 01/1999 (NBR-5688) DA ABNT, DIMENSIONADOS PARA UTILIZAÇÃO EM INSTALAÇÕES QUE FUNCIONAM POR AÇÃO DA GRAVIDADE E TEMPERATURAS INFERIORES A 50°C.

INSTALAÇÕES PREDIAIS DE ÁGUA FRIA

* TUBOS E CONEXÕES EM PVC RÍGIDO, NA COR MARROM E/OU ROSCÁVEIS PRODUZIDOS NA COR BRANCA, DE ACORDO COM A ESPECIFICAÇÃO BRASILEIRA EB892 01/1999 (NBR-5648) DA ABNT, PARA PRESSÕES MÁXIMAS DE 7,5 Kgf/cm2 (75m.c.a.) A 20°C.

OBSERVAÇÕES

01. AO COMPRAR TUBOS DE PVC PARA AS INSTALAÇÕES, VERIFICAR SE OS MESMOS CONTÉM A MARCAÇÃO COM O NÚMERO DA NORMA ABNT CORRESPONDENTE E A MARCA DO FABRICANTE, E SEMPRE PROCURAR COMPRAR TUBOS E CONEXÕES DE MESMA PROCEDÊNCIA.
02. OS TUBOS DE PVC, QUANDO EMBUTIDOS, TANTO EM ALVENARIA QUANTO NAS ESTRUTURAS DE CONCRETO, DEVERÃO FICAR TOTALMENTE INDEPENDENTES DESTAS, SEMPRE PREVENDO NESSES CASOS, FOLGA MÍNIMA DE 01(UM) DIÂMETRO ACIMA DO DIÂMETRO DA CANALIZAÇÃO.
03. PARA EXECUÇÃO DAS JUNTAS SOLDADAS E ROSCADAS, SEGUIR SEMPRE AS ESPECIFICAÇÕES E ORIENTAÇÕES DO FABRICANTE DO MATERIAL UTILIZADO.
04. AS CURVATURAS EM TUBOS DE PVC, QUANDO NECESSÁRIAS, DEVERÃO SER EXECUTADAS SEMPRE COM AS CONEXÕES APROPRIADAS, JAMAIS UTILIZAR FOGO PARA TAL FINALIDADE.
05. EM INSTALAÇÕES DE ESGOTO SANITÁRIO E ÁGUAS PLUVIAIS, NOS TRECHOS VERTICAIS JUNTO AOS PÉS-DE-COLUNA, UTILIZAR SEMPRE CURVA 87°30' COM BOLSA.
06. EM TUBULAÇÕES AÉREAS, OS TRECHOS HORIZONTAIS, O DISTANCIAMENTO DOS SUPORTES OU BRAÇADEIRAS DEVERÃO SER DE NO MÁXIMO 10(DEZ) VEZES O DIÂMETRO DOS TUBOS E NOS TRECHOS VERTICAIS ADISTÂNCIA É FIXADA EM 02(DOIS) METROS PARA TODOS OS DIÂMETROS.
07. UTILIZAR MÃO-DE-OBRA ESPECIALIZADA E QUALIFICADA PARA EXECUÇÃO DOS SERVIÇOS REFERENTES AOS SISTEMAS HIDRÁULICOS.
08. QUALQUER DÚVIDA OU PROBLEMA, CONSULTAR ANTES O ENGENHEIRO RESPONSÁVEL PELA OBRA E/OU PROJETO.

Em caso de duvidas escaneie o codigo

ou acesse: https://skfb.ly/6PwGH

LEGENDA TUBOS
AGUA FRIA
AGUA QUENTE
ALIMENTAÇÃO
ESGOTO
VENTILAÇÃO
PLUVIAL
REUSO

PROJETO HIDROSSANITÁRIO

OBRA: CONSTRUÇÃO DE UMA EDIFICAÇÃO HABITACIONAL DE 2 PAVIMENTOS EM ALVENARIA

PROPR.:

PROJETO: GEMINADAS.COM

PROJETISTA: Jeferson P. Santos

FOLHA Nº: 01/04


REVISÃO: R-01

REF.: PLANTA TERREO - SANITÁRIO/PLUVIAL
PLANTA SUPERIOR - SANITÁRIO/PLUVIAL
DETALHES GENÉRICOS - SANITÁRIO/PLUVIAL


DATA: 01/2020

Legenda
Adaptador para bocal retangular c/ terminação
Adaptador para bocal semi-circular c/ terminação
Cabeceira retangular
Curva 90 curta- coluna
Curva 90 curta- desce
Curva 90 longa
Esquadro externo retangular
Luva simples- coluna
Terminal de ventilação- coluna

Lista de Materiais		
Pluvial		
Calha metálica		
Adaptador para bocal retangular		
100 mm x 100 mm - 75 mm	2 pç	
300 mm x 150 mm - 100 mm	1 pç	
Adaptador para bocal semi-circular		
300 mm x 150 mm	1 pç	
Cabeceira retangular		
100 mm x 100 mm	2 pç	
300 mm x 150 mm	7 pç	
Calha retangular		
300 mm x 150 mm	24.43 m	
Calha semi-circular		
100 mm	1 m	
Esquadro externo retangular		
300 mm x 150 mm	1 pç	
PVC Esgoto		
Curva 90 curta		
100 mm	8 pç	
Curva 90 longa		
100 mm	1 pç	
Luva simples		
100 mm	1 pç	
Tubo rígido c/ ponta lisa		
100 mm - 4"	14.93 m	
Ventilação		
PVC Esgoto		
Terminal de ventilação		
50 mm	3 pç	
Tubo rígido c/ ponta lisa		
50 mm - 2"	17.91 m	

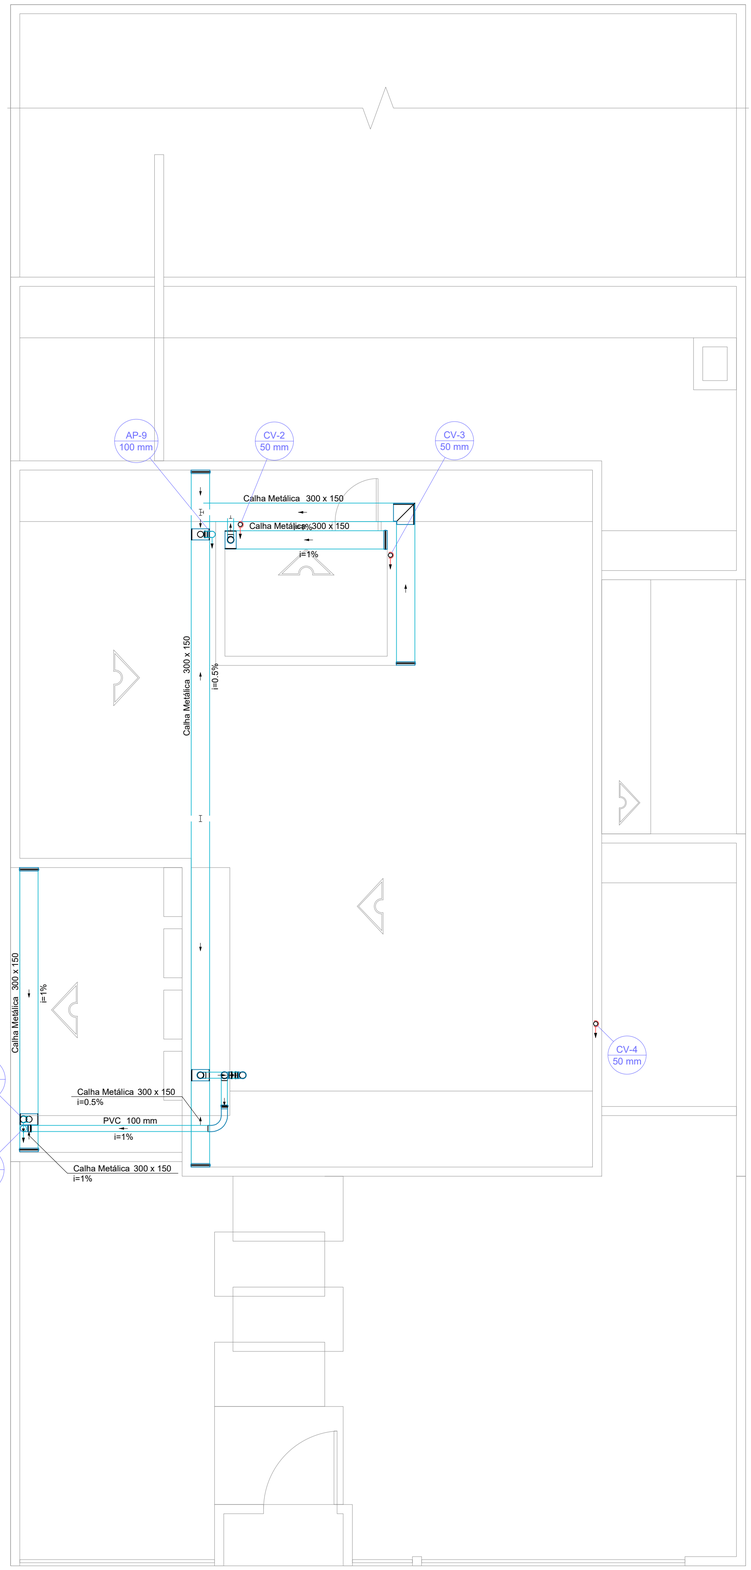

PLANTA COBERTURA - SANITÁRIO/PLUVIAL
Escala 1:50

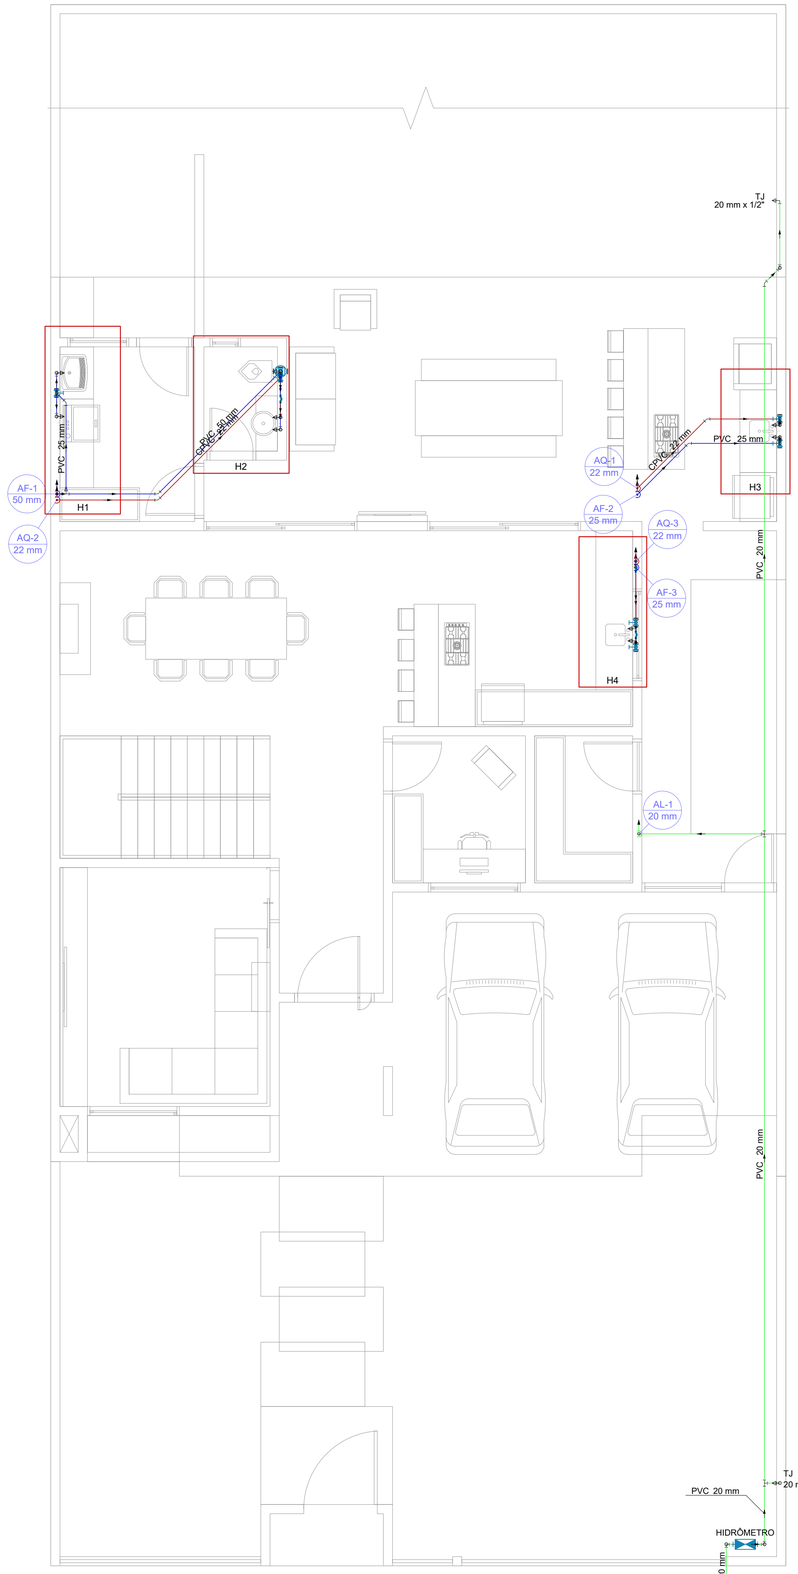

PLANTA TERREO - HIDRÁULICO
Escala 1:50

Lista de Materiais		
Água fria		
Aparelho		
Máquina de Lavar Roupa		
25mm x 3/4"	1 pç	
Torneira de Pia de Cozinha		
25 mm - 1/2"	2 pç	
Torneira de Tanque de Lavar		
25mmx 3/4"	1 pç	
Torneira de lavatório		
25 mm - 1/2"	1 pç	
Vaso Sanitário p/ Válvula de Descarga de 1 1/2"		
40mm - 1 1/2"	1 pç	
Metais		
Registro de gaveta c/ canopla cromada		
3/4"	3 pç	
Registro esfera VS compacto soldável PVC		
50 mm	1 pç	
Válvula de descarga baixa pressão		
1.1/2"	1 pç	
PVC Acessórios		
Bolsa de ligação p/ vaso sanitário		
1.1/2"	1 pç	
Engate flexível plástico		
1/2 - 30cm	1 pç	
Tubo de descarga VDE.		
38 mm	1 pç	
Tubo de ligação latão cromado c/ canopla p/ vaso Sa.		
38 mm	1 pç	
PVC rígido soldável		
Adapt sold.curto c/bolsa-rosca p registro		
25 mm - 3/4"	6 pç	
50 mm - 1.1/2"	1 pç	
Curva 45 soldável		
25 mm	2 pç	
Curva 90 soldável		
25 mm	8 pç	
50 mm	2 pç	
Curva de transposição		
25 mm	2 pç	
Joelho 45 soldável		
50 mm	1 pç	
Joelho 90° soldável		
25 mm	3 pç	
Luva soldável		
25 mm	1 pç	
Tubos		
25 mm	16.99 m	
50 mm	5.96 m	
Tê 90 soldável		
25 mm	1 pç	
Tê de redução 90 soldável		
50 mm - 25 mm	2 pç	
PVC soldável azul c/ bucha latão		
Joelho 90° soldável com bucha de latão		
25 mm - 3/4"	2 pç	
Joelho de redução 90° soldável com bucha de latão		
25 mm- 1/2"	3 pç	
Água quente		
CPVC Aquatherm		
Conector		
22 x 3/4"	6 pç	
Curva 90		
22 mm	7 pç	
Curva de transposição		
22 mm	3 pç	
Joelho 45		
22 mm	2 pç	
Joelho 90		
22 mm	4 pç	
Joelho 90° de transição		
22 x 1/2"	3 pç	
Luva		
22 mm	1 pç	
Tubo CPVC 3 Mts		
22 mm	17.35 m	
Metais		
Registro de gaveta c/ canopla cromada		
3/4"	3 pç	
PVC Acessórios		
Engate flexível cobre cromado com canopla		
1/2 - 30cm	1 pç	

Lista de Materiais	
Alimentação	
Aparelho	
Torneira de Jardim	
20mm x 1/2"	2 pç
Metais	
Registro de esfera	
1/2"	1 pç
Registro esfera borboleta bruto PVC	
1/2"	1 pç
PVC misto soldável	
Colar de tomada em PVC	
1/2"	1 pç
Joelho 90 soldável c/ rosca	
20 mm - 1/2"	4 pç
PVC rígido roscável	
Tubos	
1/2"	0.28 m
PVC rígido soldável	
Adapt sold.curto c/bolsa-rosca p registro	
20 mm - 1/2"	2 pç
Curva 45 soldável	
20 mm	1 pç
Curva 90 soldável	
20 mm	8 pç
Joelho 90° soldável	
20 mm	1 pç
Luva soldável	
20 mm	1 pç
Tubos	
20 mm	30.79 m
Tê 90 soldável	
20 mm	2 pç
PVC soldável azul c/ bucha latão	
Joelho 90° soldável com bucha de latão	
20 mm - 1/2"	2 pç

Legenda
Alimentador Predial
Curva de transposição
Hidrômetros
Registro de gaveta c/canopla cromada c/ CPVC
Registro de gaveta c/canopla cromada c/PVC soldável
Registro esfera VS compacto soldável
Valvula de descarga c/PVC soldável

INSTALAÇÕES PREDIAIS DE ESGOTO SANITÁRIO

* TUBOS E CONEXÕES EM PVC RÍGIDO, NA COR BRANCA, PARA INSTALAÇÕES PREDIAIS DE ESGOTO SANITÁRIO E VENTILAÇÃO, FABRICADOS DE ACORDO COM A ESPECIFICAÇÃO BRASILEIRA EB608 01/1999 (NBR-5688) DA ABNT, DIMENSIONADOS PARA UTILIZAÇÃO EM INSTALAÇÕES QUE FUNCIONAM POR AÇÃO DA GRAVIDADE E TEMPERATURAS INFERIORES A 50°C.

INSTALAÇÕES PREDIAIS DE ÁGUA FRIA

* TUBOS E CONEXÕES EM PVC RÍGIDO, NA COR MARROM E/OU ROSCÁVEIS PRODUZIDOS NA COR BRANCA, DE ACORDO COM A ESPECIFICAÇÃO BRASILEIRA EB892 01/1999 (NBR-5648) DA ABNT, PARA PRESSÕES MÁXIMAS DE 7,5 Kgf/cm2 (75m.c.a.) A 20°C.

OBSERVAÇÕES

01. AO COMPRAR TUBOS DE PVC PARA AS INSTALAÇÕES, VERIFICAR SE OS MESMOS CONTÉM A MARCAÇÃO COM O NÚMERO DA NORMA ABNT CORRESPONDENTE E A MARCA DO FABRICANTE, É SEMPRE PROCURAR COMPRAR TUBOS E CONEXÕES DE MESMA PROCEDÊNCIA.
02. OS TUBOS DE PVC, QUANDO EMBUTIDOS, TANTO EM ALVENARIA QUANTO NAS ESTRUTURAS DE CONCRETO, DEVERÃO FICAR TOTALMENTE INDEPENDENTES DESTAS, SEMPRE PREVENDO NESSES CASOS, FOLGA MÍNIMA DE 01(UM) DIÂMETRO ACIMA DO DIÂMETRO DA CANALIZAÇÃO.
03. PARA EXECUÇÃO DAS JUNTAS SOLDADAS E ROSCADAS, SEGUIR SEMPRE AS ESPECIFICAÇÕES E ORIENTAÇÕES DO FABRICANTE DO MATERIAL UTILIZADO.
04. AS CURVATURAS EM TUBOS DE PVC, QUANDO NECESSÁRIAS, DEVERÃO SER EXECUTADAS SEMPRE COM AS CONEXÕES APROPRIADAS, JAMAIS UTILIZAR FOGO PARA TAL FINALIDADE.
05. EM INSTALAÇÕES DE ESGOTO SANITÁRIO E ÁGUAS PLUVIAIS, NOS TRECHOS VERTICAIS JUNTO AOS PÉS-DE-COLUNA, UTILIZAR SEMPRE CURVA 87°30' COM BOLSA.
06. EM TUBULAÇÕES AÉREAS, OS TRECHOS HORIZONTAIS, O DISTANCIAMENTO DOS SUPORTES OU BRAÇADEIRAS DEVERÃO SER DE NO MÁXIMO 10(DEZ) VEZES O DIÂMETRO DOS TUBOS E NOS TRECHOS VERTICAIS ADISTÂNCIA É FIXADA EM 02(DOIS) METROS PARA TODOS OS DIÂMETROS.
07. UTILIZAR MÃO-DE-OBRA ESPECIALIZADA E QUALIFICADA PARA EXECUÇÃO DOS SERVIÇOS REFERENTES AOS SISTEMAS HIDRÁULICOS.
08. QUALQUER DÚVIDA OU PROBLEMA, CONSULTAR ANTES O ENGENHEIRO RESPONSÁVEL PELA OBRA E/OU PROJETO.

Em caso de duvidas escaneie o codigo

ou acesse: https://skfb.ly/6PwGH

LEGENDA TUBOS
AGUA-FRIA
AGUA-QUENTE
ALIMENTAÇÃO
ESGOTO
VENTILAÇÃO
PLUVIAL
REUSO

PROJETO HIDROSSANITÁRIO

OBRA: CONSTRUÇÃO DE UMA EDIFICAÇÃO HABITACIONAL DE 2 PAVIMENTOS EM ALVENARIA

PROPR.:

PROJETO: GEMINADAS.COM

PROJETO: Jeferson P. Santos

FOLHA Nº: 02/04


REVISÃO: R-01

REF.: PLANTA COBERTURA - SANITÁRIO/PLUVIAL
PLANTA TERREO - HIDRÁULICO


DATA: 01/2020

Legenda
Curva de transposição
Registro de gaveta c/canopla cromada c/ CPVC
Registro de gaveta c/canopla cromada c/PVC soldável
Registro monocomando
Valvula de descarga c/PVC soldável

Lista de Materiais	
Alimentação	
PVC rígido soldável	
Luva soldável	
20 mm	1 pç
Tubos	
20 mm	3.6 m
Água fria	
Aparelho	
Torneira de lavatório	
25 mm - 1/2"	3 pç
Vaso Sanitário p/ Válvula de Descarga de 1 1/2"	
40mm - 1 1/2"	2 pç
Metais	
Registro de gaveta c/ canopla cromada	
1.1/2"	2 pç
3/4"	2 pç
Válvula de descarga baixa pressão	
1.1/2"	2 pç
PVC Acessórios	
Bolsa de ligação p/ vaso sanitário	
1.1/2"	2 pç
Engate flexível plástico	
1/2 - 30cm	3 pç
Tubo de descarga VDE.	
38 mm	2 pç
Tubo de ligação latão cromado c/ canopla p/ vaso Sa.	
38 mm	2 pç
PVC rígido soldável	
Adapt sold.curto c/bolsa-rosca p registro	
25 mm - 3/4"	4 pç
50 mm - 1.1/2"	6 pç
Curva 90 soldável	
25 mm	4 pç
Curva de transposição	
25 mm	1 pç
Luva soldável	
25 mm	4 pç
50 mm	3 pç
Tubos	
25 mm	15.01 m
50 mm	7.17 m
Tê 90 soldável	
25 mm	2 pç
Tê de redução 90 soldável	
50 mm - 25 mm	1 pç
PVC soldável azul c/ bucha latão	
Joelho de redução 90° soldável com bucha de latão	
25 mm- 1/2"	3 pç
Água quente	
Aparelho	
Chuveiro	
22mm x 1/2"	2 pç
CPVC Aquatherm	
Conector	
22 x 3/4"	6 pç
Curva 90	
22 mm	2 pç
Curva de transposição	
22 mm	6 pç
Joelho 90	
22 mm	3 pç
Joelho 90° de transição	
22 x 1/2"	5 pç
Luva	
22 mm	6 pç
Tubo CPVC 3 Mts	
22 mm	21.16 m
Tê 90	
22 mm	2 pç
Metais	
Registro de gaveta c/ canopla cromada	
3/4"	3 pç
Registro monocomando para chuveiro	
3/4"	2 pç
PVC Acessórios	
Engate flexível cobre cromado com canopla	
1/2 - 30cm	3 pç

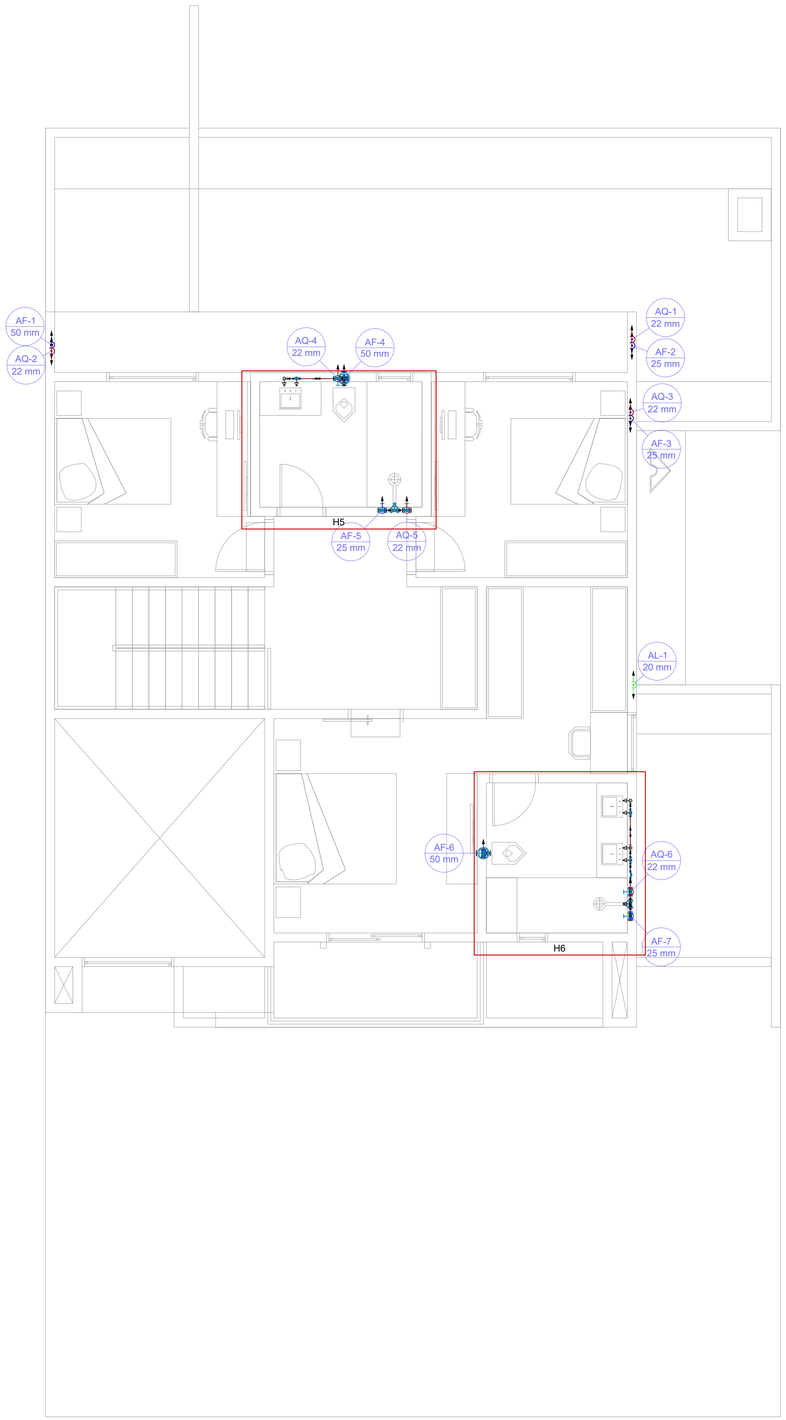

PLANTA SUPERIOR - HIDRÁULICO
Escala 1:50

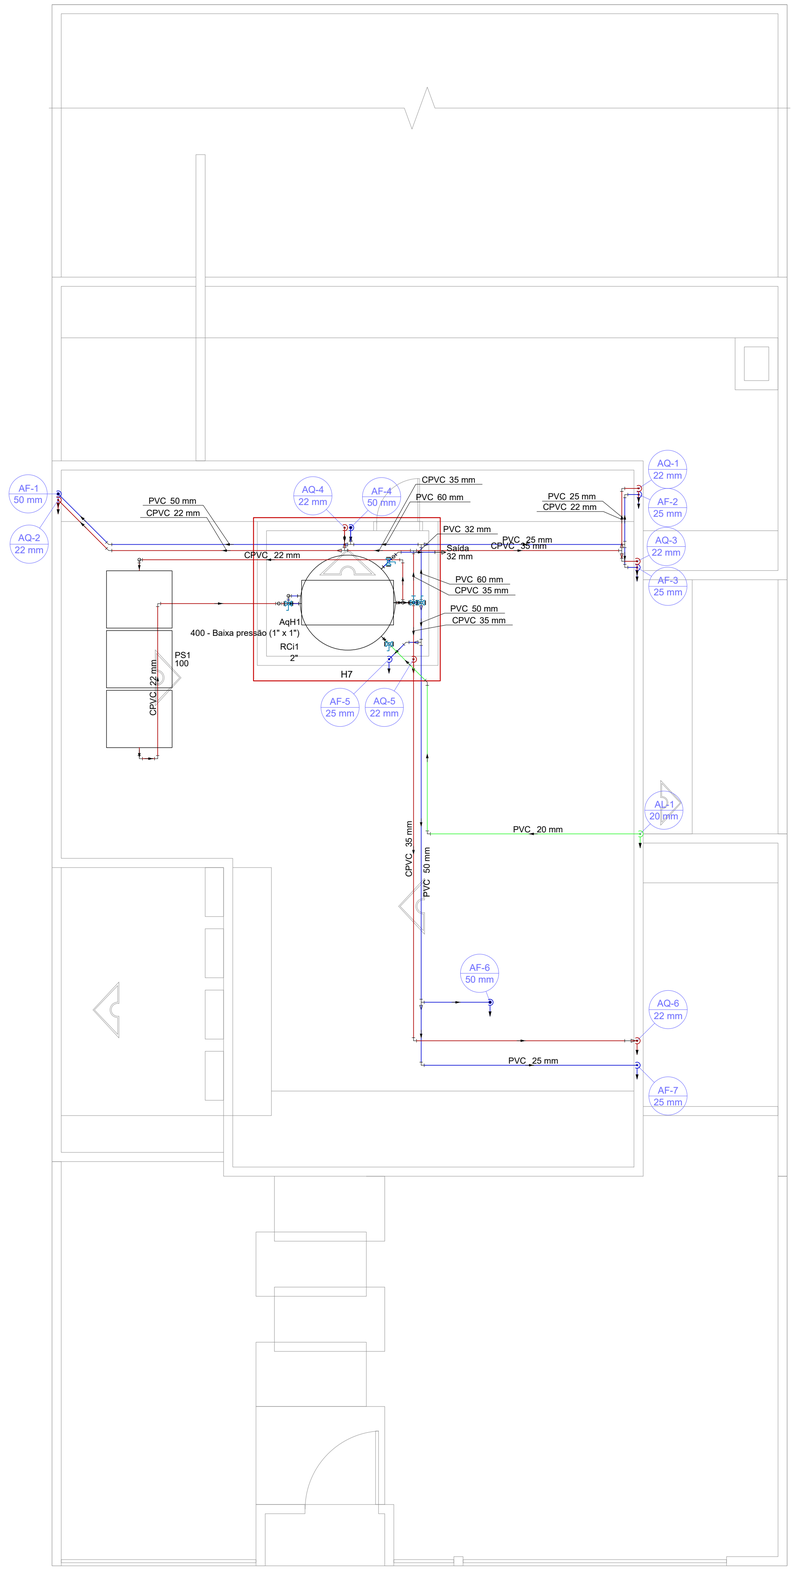

PLANTA COBERTURA - HIDRÁULICO
Escala 1:50

Lista de Materiais	
Alimentação	
Metais	
Registro esfera VS compacto soldável PVC	
20 mm	1 pç
PVC rígido soldável	
Adapt sold. c/ flange livre p/ cx. d´água	
20 mm - 1/2"	1 pç
Curva 45 soldável	
20 mm	1 pç
Curva 90 soldável	
20 mm	4 pç
Torneira de bóia	
1/2"	1 pç
Tubos	
20 mm	9.7 m
Água fria	
Metais	
Registro esfera VS compacto soldável PVC	
25 mm	1 pç
32 mm	1 pç
60 mm	1 pç
PVC rígido soldável	
Adapt sold. c/ flange livre p/ cx. d´água	
25 mm - 3/4"	1 pç
32 mm - 1"	2 pç
60 mm - 2"	2 pç
Bucha de redução sold. curta	
60 mm - 50 mm	3 pç
Bucha de redução sold. longa	
50 mm - 25 mm	1 pç
60 mm - 25 mm	1 pç
Curva 45 soldável	
25 mm	1 pç
32 mm	1 pç
Curva 90 soldável	
25 mm	7 pç
32 mm	1 pç
50 mm	3 pç
60 mm	1 pç
Joelho 45 soldável	
50 mm	1 pç
Joelho 90° soldável	
25 mm	4 pç
Tubos	
25 mm	12.8 m
32 mm	1.98 m
50 mm	13.3 m
60 mm	3.6 m
Tê 90 soldável	
25 mm	1 pç
32 mm	1 pç
50 mm	1 pç
60 mm	3 pç
Tê de redução 90 soldável	
50 mm - 25 mm	1 pç
Reservatório cilindrico	
Polietileno	
1500 L	1 pç

Lista de Materiais	
Água quente	
CPVC Aquatherm	
Bucha de redução	
35 x 22	3 pç
Conector	
35 x 1.1/4"	2 pç
Curva 90	
22 mm	17 pç
Joelho 45	
22 mm	1 pç
Joelho 90	
35 mm	2 pç
Tubo CPVC 3 Mts	
22 mm	24.75 m
35 mm	16.99 m
Tê 90	
35 mm	2 pç
Tê de Redução	
35 x 22 mm	3 pç
Cobre	
Flange saída p/cx. d'agua	
22 mm	1 pç
35 mm	1 pç
Luva bolsa - bolsa	
22 mm	1 pç
28 mm	2 pç
Metais	
Registro de gaveta bruto ABNT	
1"1/4	1 pç
Placa Solar	
CSC Premium - Cumulus	
100	1 pç
Reservatório térmico solar	
Reservatório Solar - Horizontal	
400 L	1 pç

Legenda
Registro bruto gaveta ABNT c/ CPVC
Registro esfera VS compacto soldável

INSTALAÇÕES PREDIAIS DE ESGOTO SANITÁRIO

* TUBOS E CONEXÕES EM PVC RÍGIDO, NA COR BRANCA, PARA INSTALAÇÕES PREDIAIS DE ESGOTO SANITÁRIO E VENTILAÇÃO, FABRICADOS DE ACORDO COM A ESPECIFICAÇÃO BRASILEIRA EB608 01/1999 (NBR-5688) DA ABNT, DIMENSIONADOS PARA UTILIZAÇÃO EM INSTALAÇÕES QUE FUNCIONAM POR AÇÃO DA GRAVIDADE E TEMPERATURAS INFERIORES A 50°C.

INSTALAÇÕES PREDIAIS DE ÁGUA FRIA

* TUBOS E CONEXÕES EM PVC RÍGIDO, NA COR MARROM E/OU ROSCÁVEIS PRODUZIDOS NA COR BRANCA, DE ACORDO COM A ESPECIFICAÇÃO BRASILEIRA EB892 01/1999 (NBR-5648) DA ABNT, PARA PRESSÕES MÁXIMAS DE 7,5 Kgf/cm2 (75m.c.a.) A 20°C.

OBSERVAÇÕES

01. AO COMPRAR TUBOS DE PVC PARA AS INSTALAÇÕES, VERIFICAR SE OS MESMOS CONTÉM A MARCAÇÃO COM O NÚMERO DA NORMA ABNT CORRESPONDENTE E A MARCA DO FABRICANTE, E SEMPRE PROCURAR COMPRAR TUBOS E CONEXÕES DE MESMA PROCEDÊNCIA.
02. OS TUBOS DE PVC, QUANDO EMBUTIDOS, TANTO EM ALVENARIA QUANTO NAS ESTRUTURAS DE CONCRETO, DEVERÃO FICAR TOTALMENTE INDEPENDENTES DESTAS, SEMPRE PREVENDO NESSES CASOS, FOLGA MÍNIMA DE 01(UM) DIÂMETRO ACIMA DO DIÂMETRO DA CANALIZAÇÃO.
03. PARA EXECUÇÃO DAS JUNTAS SOLDADAS E ROSCADAS, SEGUIR SEMPRE AS ESPECIFICAÇÕES E ORIENTAÇÕES DO FABRICANTE DO MATERIAL UTILIZADO.
04. AS CURVATURAS EM TUBOS DE PVC, QUANDO NECESSÁRIAS, DEVERÃO SER EXECUTADAS SEMPRE COM AS CONEXÕES APROPRIADAS, JAMAIS UTILIZAR FOGO PARA TAL FINALIDADE.
05. EM INSTALAÇÕES DE ESGOTO SANITÁRIO E ÁGUAS PLUVIAIS, NOS TRECHOS VERTICAIS JUNTO AOS PÉS-DE-COLUNA, UTILIZAR SEMPRE CURVA 87°30' COM BOLSA.
06. EM TUBULAÇÕES AÉREAS, OS TRECHOS HORIZONTAIS, O DISTANCIAMENTO DOS SUPORTES OU BRAÇADEIRAS DEVERÃO SER DE NO MÁXIMO 10(DEZ) VEZES O DIÂMETRO DOS TUBOS E NOS TRECHOS VERTICAIS ADISTÂNCIA É FIXADA EM 02(DOIS) METROS PARA TODOS OS DIÂMETROS.
07. UTILIZAR MÃO-DE-OBRA ESPECIALIZADA E QUALIFICADA PARA EXECUÇÃO DOS SERVIÇOS REFERENTES AOS SISTEMAS HIDRÁULICOS.
08. QUALQUER DÚVIDA OU PROBLEMA, CONSULTAR ANTES O ENGENHEIRO RESPONSÁVEL PELA OBRA E/OU PROJETO.

Em caso de duvidas
escaneie o codigo

ou acesse: https://skfb.ly/6PwGH

LEGENDA TUBOS
- AGUA FRIA
- AGUA QUENTE
- ALIMENTAÇÃO
- ESGOTO
- VENTILAÇÃO
- PLUVIAL
- REUSO

PROJETO HIDROSSANITÁRIO

OBRA: CONSTRUÇÃO DE UMA EDIFICAÇÃO HABITACIONAL DE 2 PAVIMENTOS EM ALVENARIA

PROPR.:

PROJETO:

GEMINADAS.COM


RESPONSÁVEL: Jeferson P. Santos

FOLHA Nº: 03/04


REVISÃO: R-01

REF.: PLANTA SUPERIOR - HIDRÁULICO
PLANTA COBERTURA - HIDRÁULICO


DATA: 01/2020

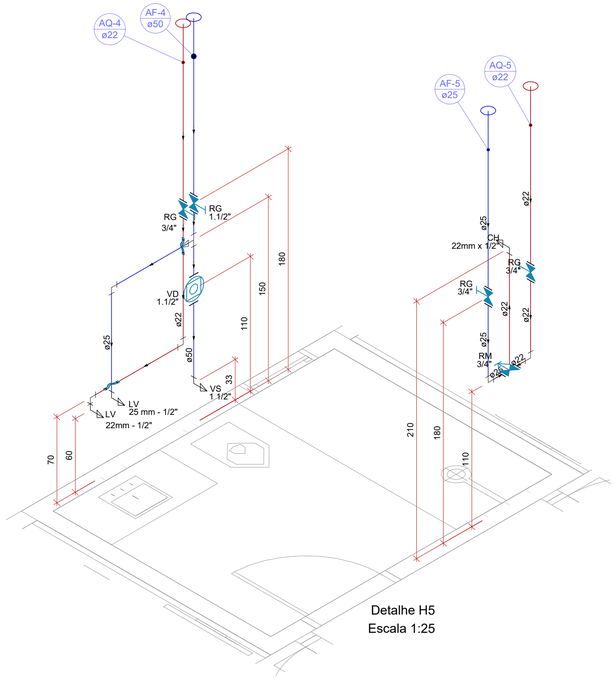


Detalhe H5
Escala 1:25

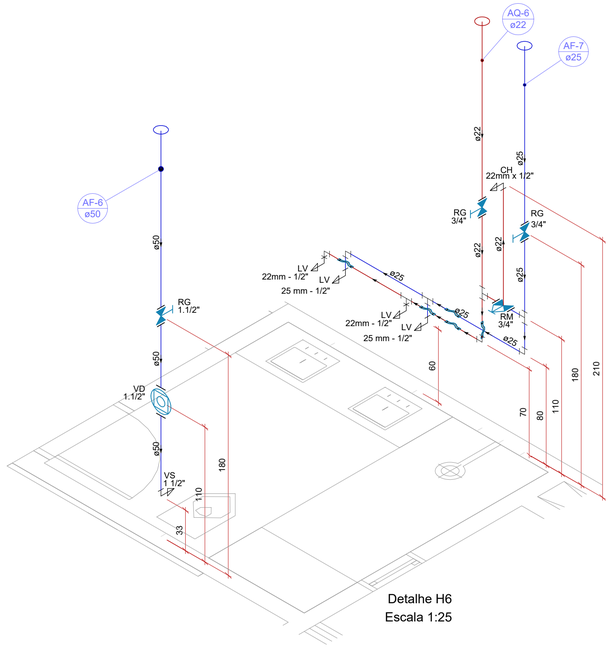


Detalhe H6
Escala 1:25

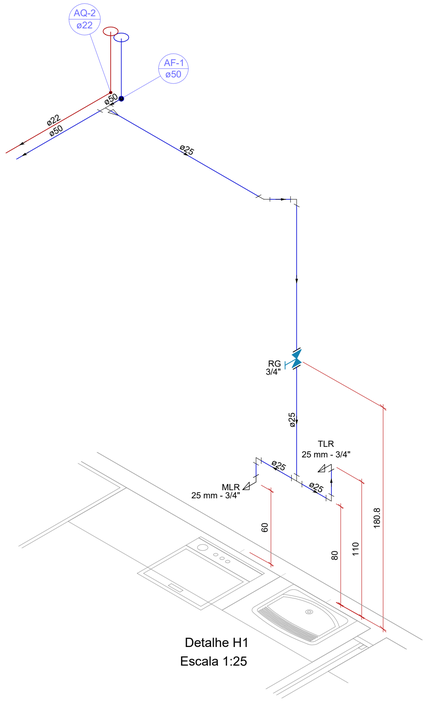

Detalhe H1
Escala 1:25

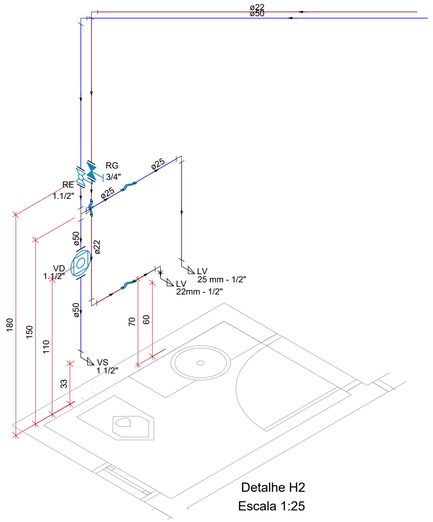


Detalhe H2
Escala 1:25

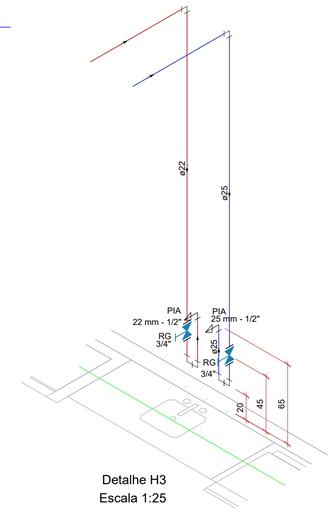


Detalhe H3
Escala 1:25

Detalhe H7
Escala 1:25

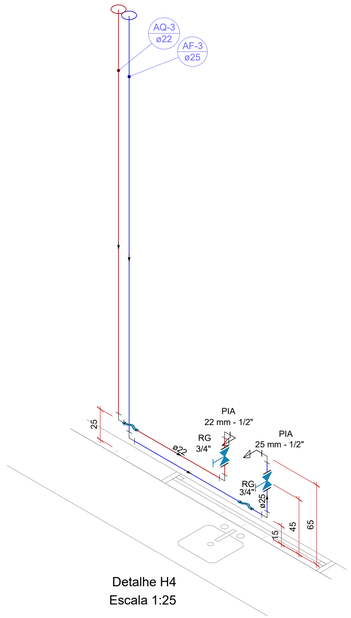

Detalhe H4
Escala 1:25

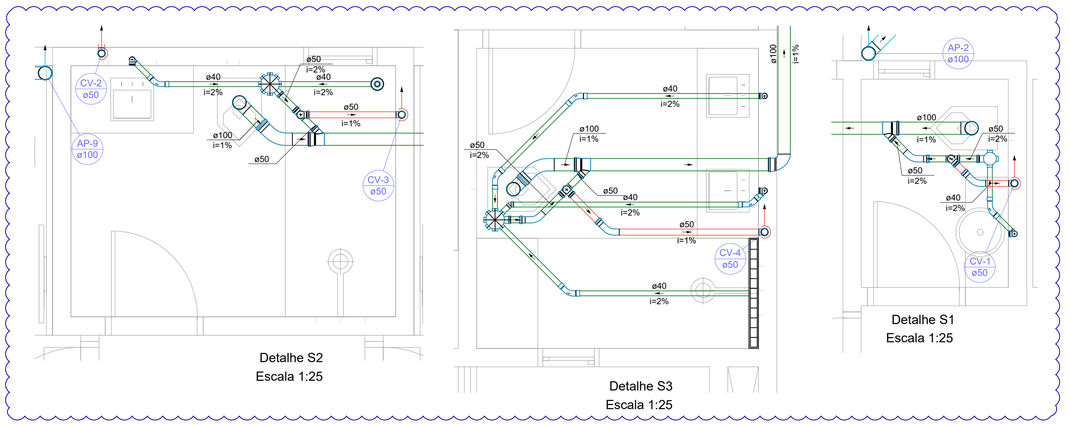

Detalhe S2
Escala 1:25

Detalhe S3
Escala 1:25

Detalhe S1
Escala 1:25

Em caso de duvidas escaneie o codigo

ou acesse: https://skfb.ly/6PwGH

LEGENDA TUBOS

- AGUA-FRIA
- AGUA-QUENTE
- ALIMENTAÇÃO
- ESGOTO
- VENTILAÇÃO
- PLUVIAL
- RELIGO

INSTALAÇÕES PREDIAIS DE ESGOTO SANITÁRIO

* TUBOS E CONEXÕES EM PVC RÍGIDO, NA COR BRANCA, PARA INSTALAÇÕES PREDIAIS DE ESGOTO SANITÁRIO E VENTILAÇÃO, FABRICADOS DE ACORDO COM A ESPECIFICAÇÃO BRASILEIRA EB608 01/1999 (NBR-5688) DA ABNT, DIMENSIONADOS PARA UTILIZAÇÃO EM INSTALAÇÕES QUE FUNCIONAM POR AÇÃO DA GRAVIDADE E TEMPERATURAS INFERIORES A 50°C.

INSTALAÇÕES PREDIAIS DE ÁGUA FRIA

* TUBOS E CONEXÕES EM PVC RÍGIDO, NA COR MARROM E/OU ROSCÁVEIS PRODUZIDOS NA COR BRANCA, DE ACORDO COM A ESPECIFICAÇÃO BRASILEIRA EB892 01/1999 (NBR-5648) DA ABNT, PARA PRESSÕES MÁXIMAS DE 7,5 Kgf/cm2 (75m.c.a.) A 20°C.

OBSERVAÇÕES

01. AO COMPRAR TUBOS DE PVC PARA AS INSTALAÇÕES, VERIFICAR SE OS MESMOS CONTÉM A MARCAÇÃO COM O NÚMERO DA NORMA ABNT CORRESPONDENTE E A MARCA DO FABRICANTE. É SEMPRE PROCURAR COMPRAR TUBOS E CONEXÕES DE MESMA PROCEDÊNCIA.
02. OS TUBOS DE PVC, QUANDO EMBUTIDOS, TANTO EM ALVENARIA QUANTO NAS ESTRUTURAS DE CONCRETO, DEVERÃO FICAR TOTALMENTE INDEPENDENTES DESTAS, SEMPRE PREVENDO NESSES CASOS, FOLGA MÍNIMA DE 01(UM) DIÂMETRO ACIMA DO DIÂMETRO DA CANALIZAÇÃO.
03. PARA EXECUÇÃO DAS JUNTAS SOLDADAS E ROSCADAS, SEGUIR SEMPRE AS ESPECIFICAÇÕES E ORIENTAÇÕES DO FABRICANTE DO MATERIAL UTILIZADO.
04. AS CURVATURAS EM TUBOS DE PVC, QUANDO NECESSÁRIAS, DEVERÃO SER EXECUTADAS SEMPRE COM AS CONEXÕES APROPRIADAS, JAMAIS UTILIZAR FOGO PARA TAL FINALIDADE.
05. EM INSTALAÇÕES DE ESGOTO SANITÁRIO E ÁGUAS PLUVIAIS, NOS TRECHOS VERTICAIS JUNTO AOS PÉS-DE-COLUNA, UTILIZAR SEMPRE CURVA 87°30' COM BOLSA.
06. EM TUBULAÇÕES AÉREAS, OS TRECHOS HORIZONTAIS, O DISTANCIAMENTO DOS SUPORTES OU BRAÇADEIRAS DEVERÃO SER DE NO MÁXIMO 10(DEZ) VEZES O DIÂMETRO DOS TUBOS E NOS TRECHOS VERTICAIS ADISTÂNCIA É FIXADA EM 02(DOIS) METROS PARA TODOS OS DIÂMETROS.
07. UTILIZAR MÃO-DE-OBRA ESPECIALIZADA E QUALIFICADA PARA EXECUÇÃO DOS SERVIÇOS REFERENTES AOS SISTEMAS HIDRÁULICOS.
08. QUALQUER DÚVIDA OU PROBLEMA, CONSULTAR ANTES O ENGENHEIRO RESPONSÁVEL PELA OBRA E/OU PROJETO.

PROJETO HIDROSSANITÁRIO

OBRA: CONSTRUÇÃO DE UMA EDIFICAÇÃO HABITACIONAL DE 2 PAVIMENTOS EM ALVENARIA

PROPR.:

PROJETO: GEMINADAS.COM

DESENH.: Jeferson P. Santos

FOLHA Nº: 04/04

REVISÃO: R-01

REF.: DETALHES ISOMÉTRICOS - HIDRÁULICO
DETALHES - SANITÁRIO/PLUVIAL

DATA: 01/2020